

PONTE dalla scheda segnale (J1) e bulk locali

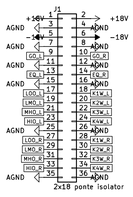





ISOLATOR lato L (incroci C, dec. 152; iso-incc-banca.inc)

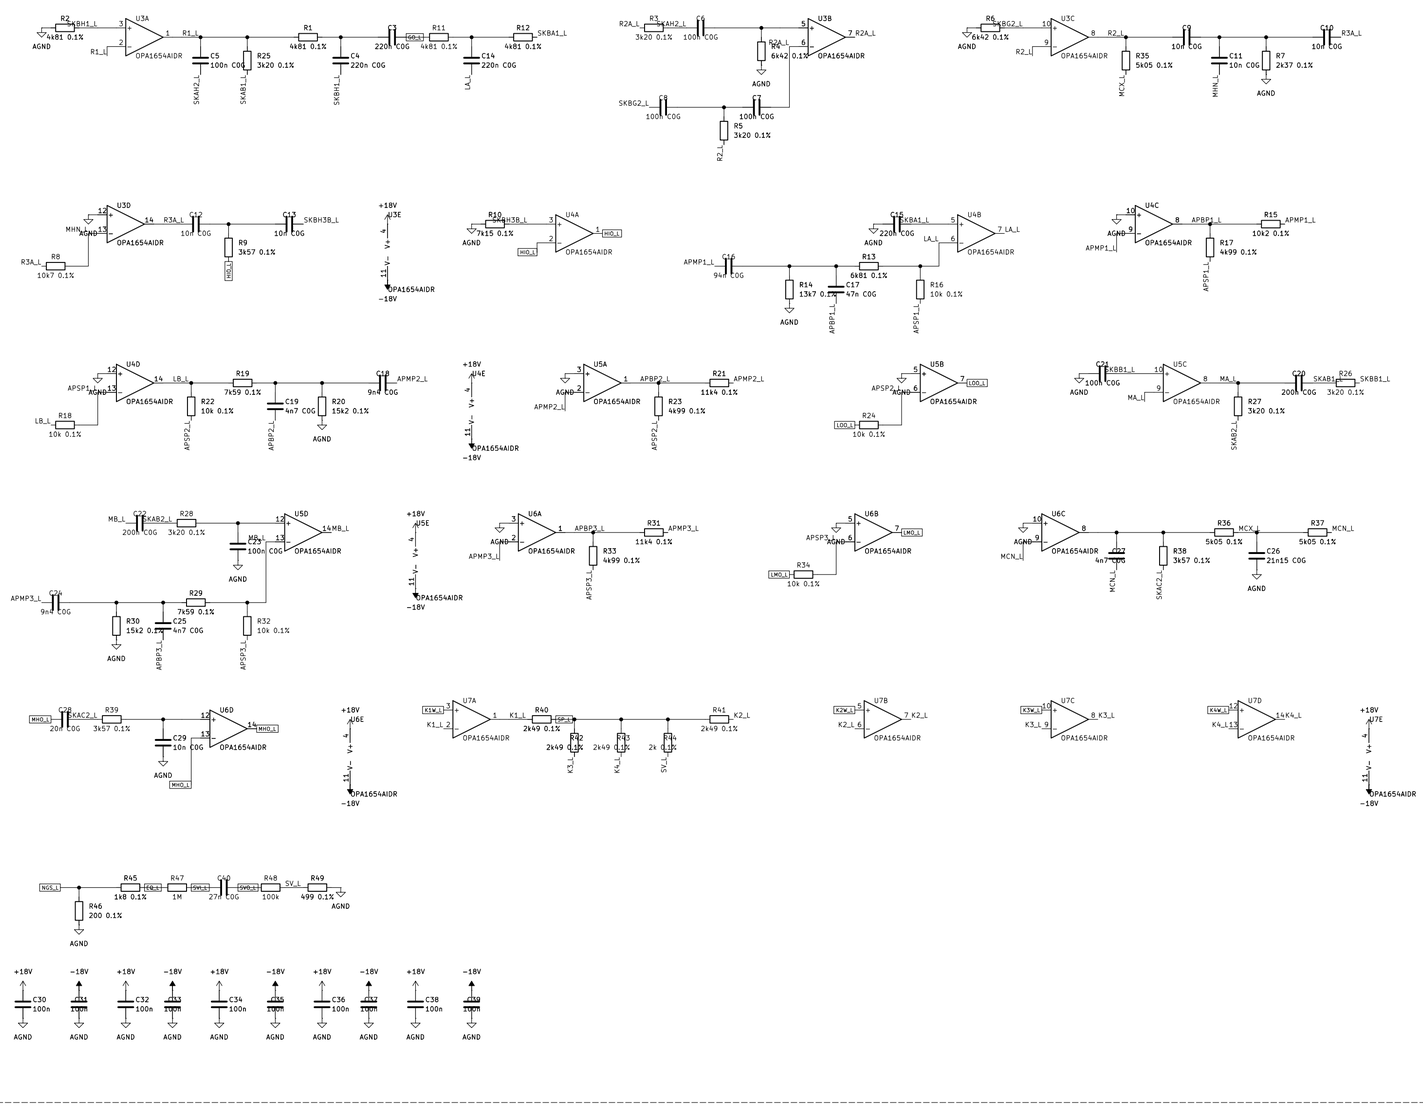

ISOLATOR lato R (incroci C, dec. 152; iso-incc-banca.inc)

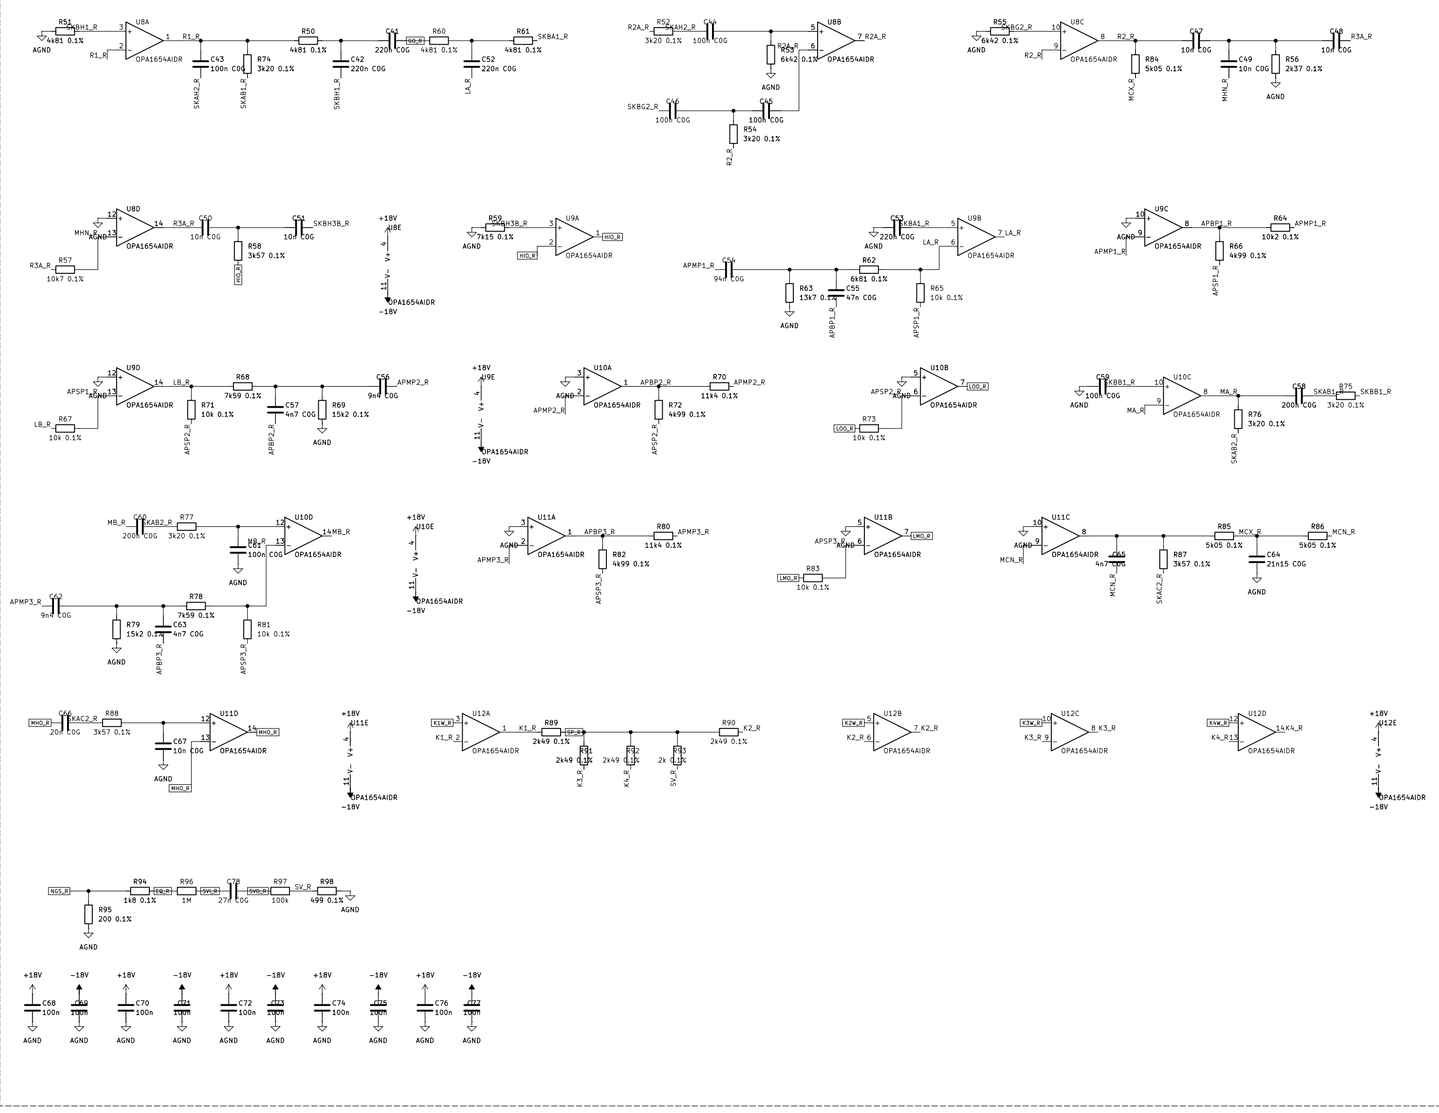

SOMMA DELL'ISOLATOR (non invertente) e SERVO DC

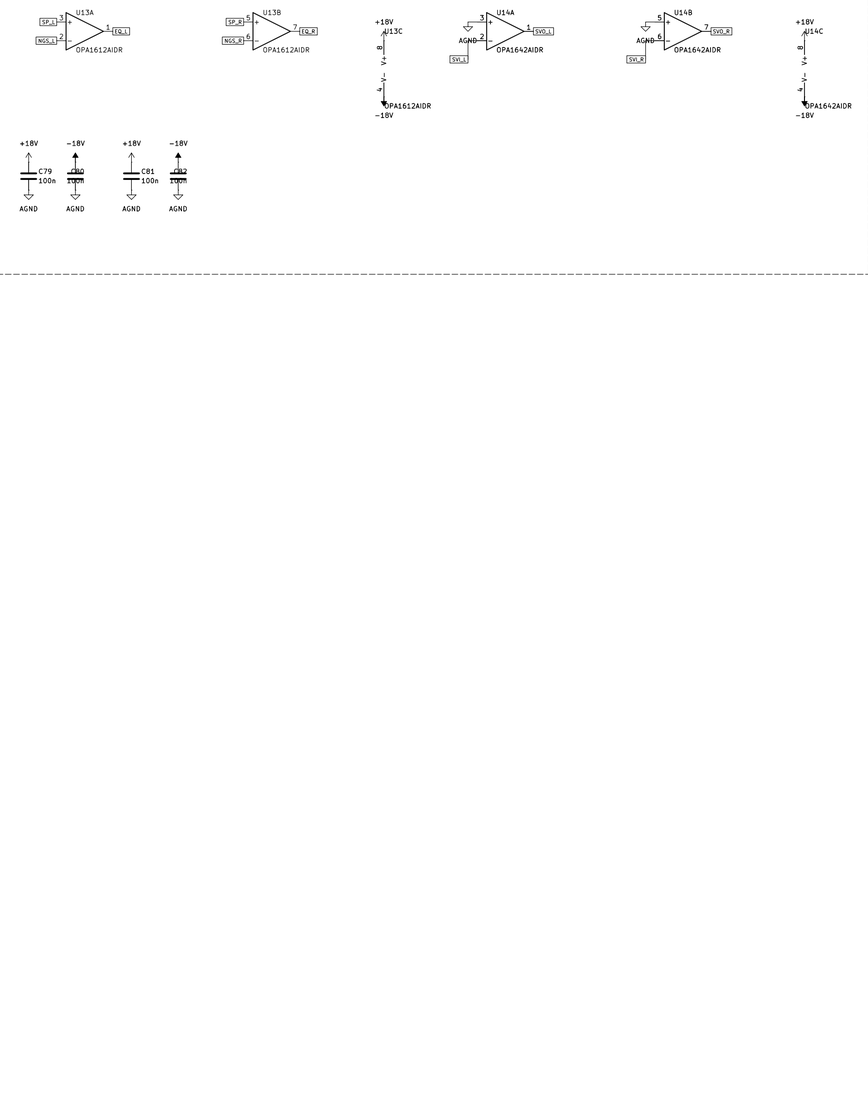

PWR_FLAG (per il controllo ERC)



Generato da pcb/tools/leggibile.py dallo stesso netlist della PCB: non modificare a mano

Sheet: /
File: canale-isolator.kicad_sch

Title: maelcum CANALE isolator (dec. 152) – bozza v0.1 – schema leggibile

Size: User	Date:	Rev: 0.1-bozza
KiCad E.D.A. 10.0.7		Id: 1/1